改　修　図

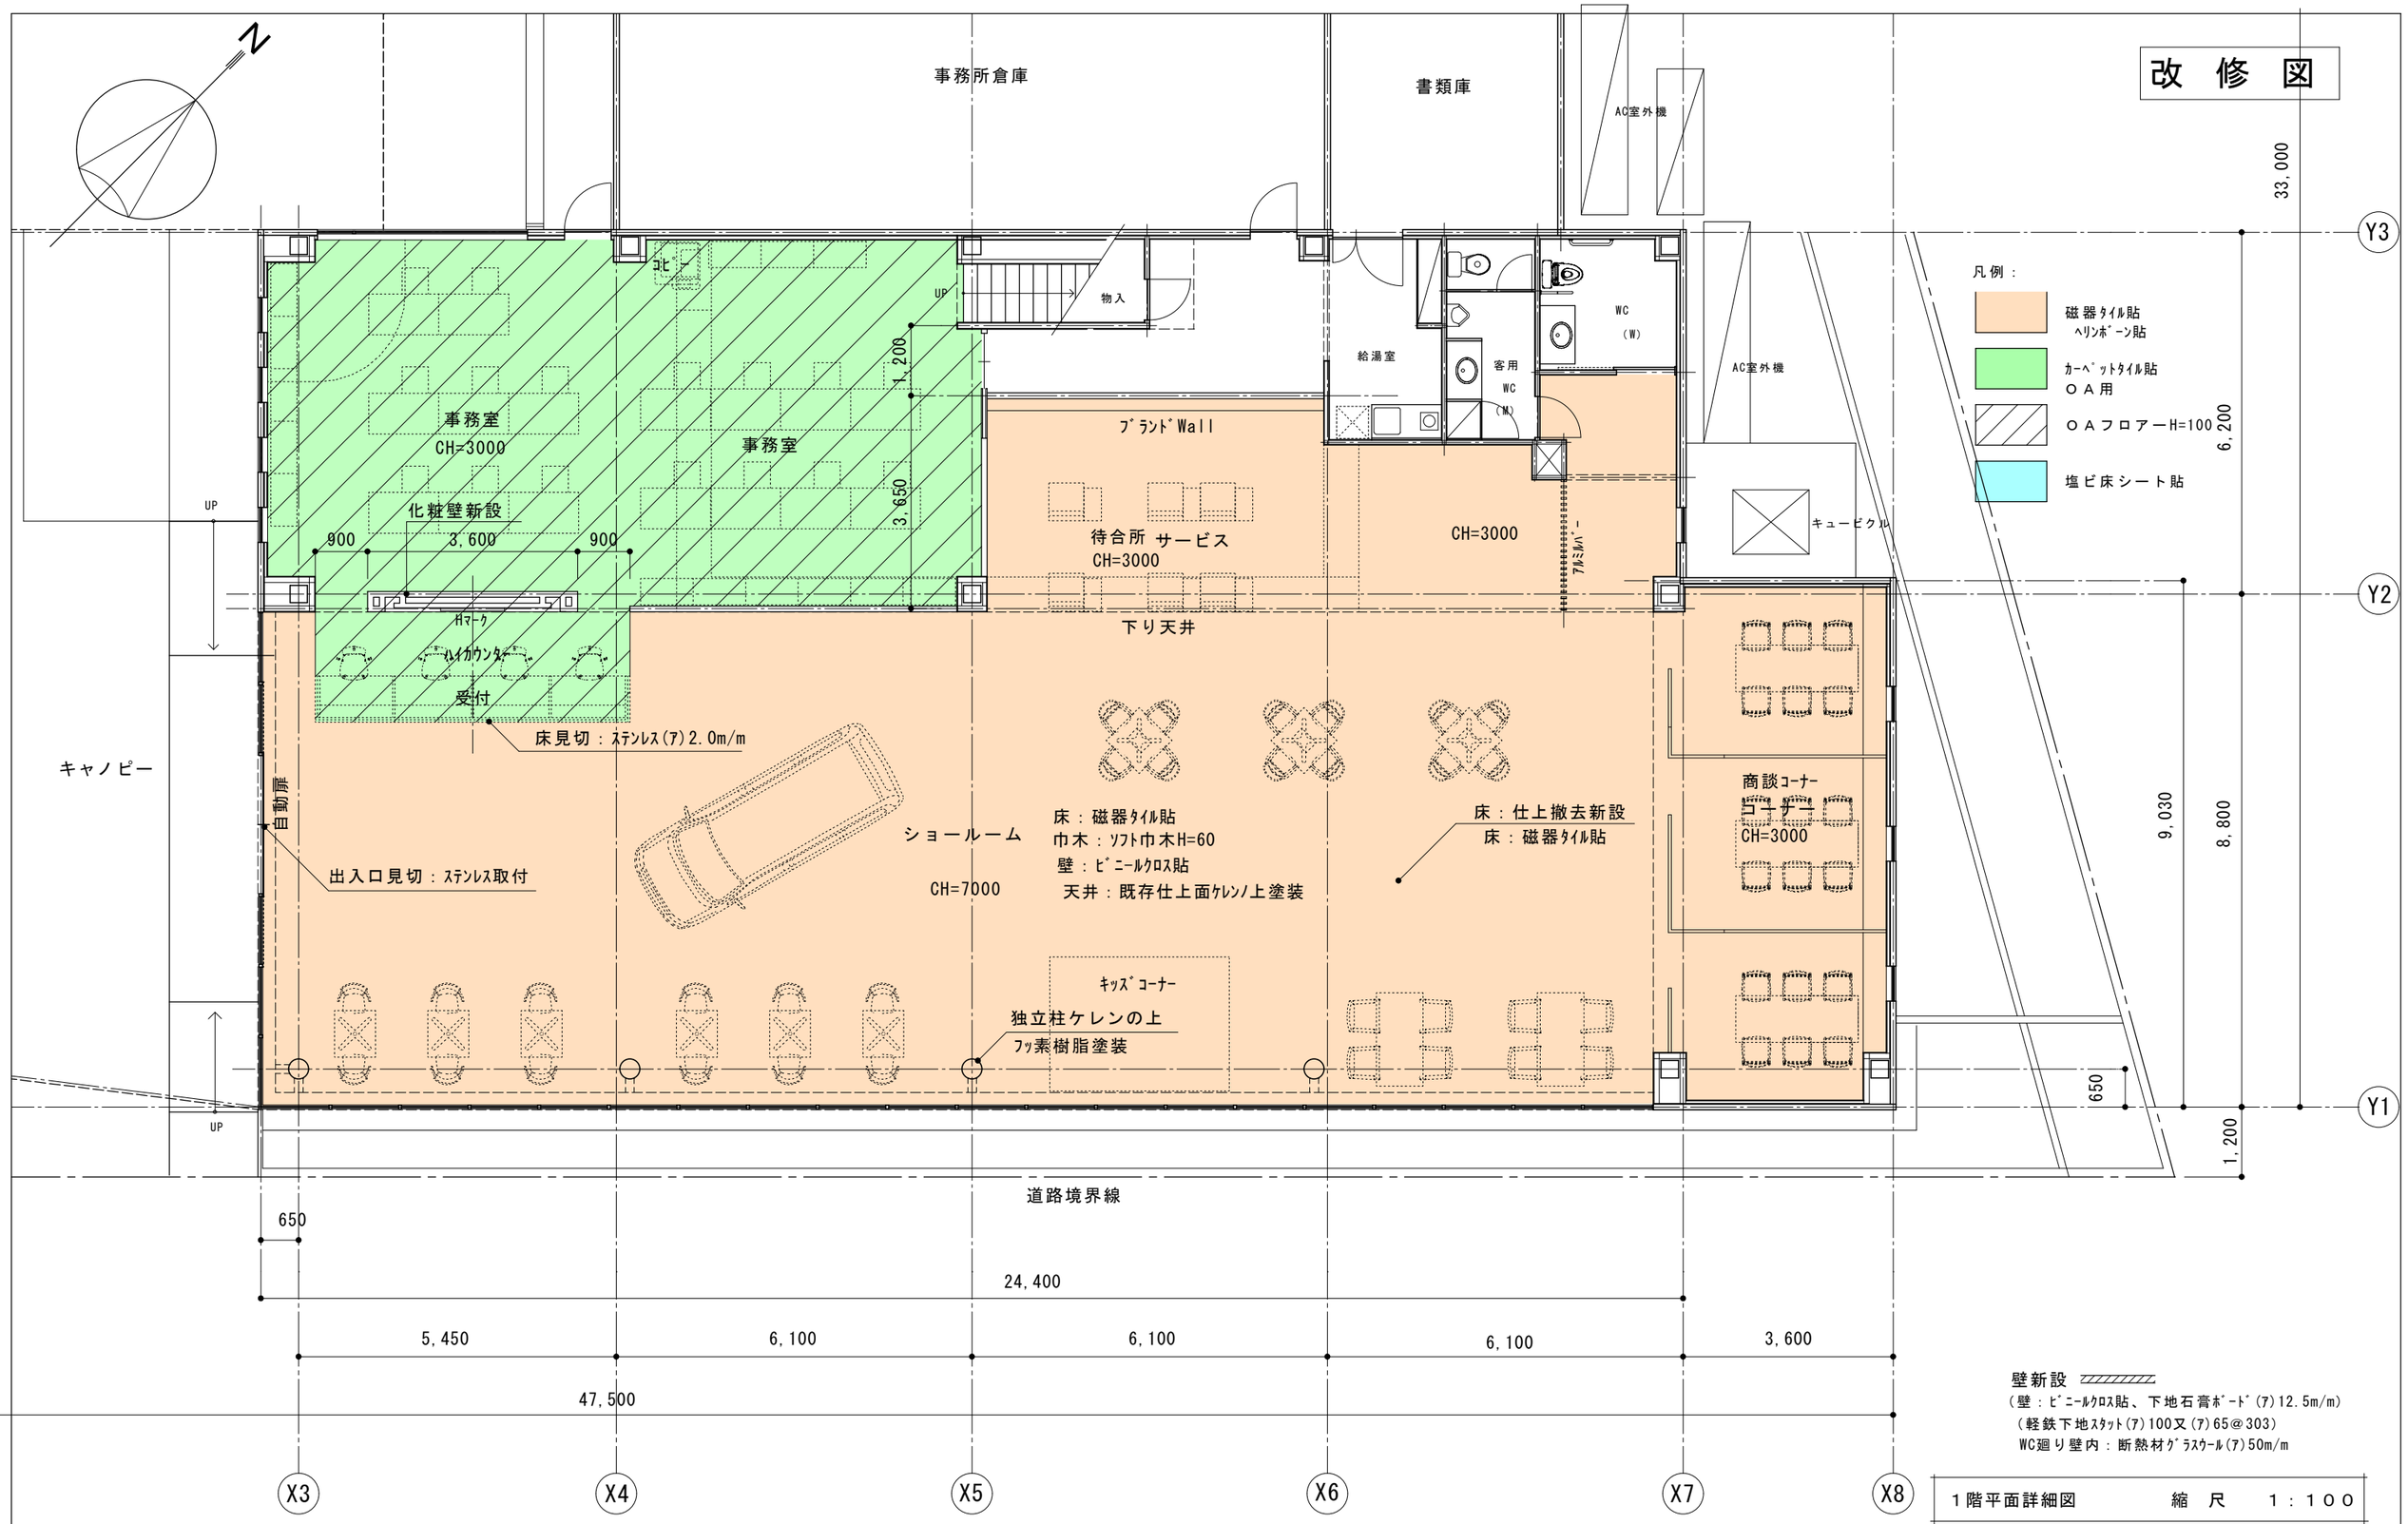

壁新設
（壁：ﾋﾞﾆｰﾙｸﾛｽ貼、下地石膏ﾎﾞｰﾄﾞ(ｱ)12.5m/m）
（軽鉄下地ｽﾀｯﾄ(ｱ)100又(ｱ)65@303）
WC廻り壁内：断熱材ｸﾞﾗｽｳｰﾙ(ｱ)50m/m

1階平面詳細図	縮　尺	1：100

＊既存取合い現場実測の事
＊既存建築撤去部分は復旧の事。

OFFICE		ARCHITECT	DATE	PROJECT	TITLE	SCALE	NO
0−1Design	東京都 知事登録 第65913号 ０−１設計株式会社 一級建築士事務所 114-0011 東京都北区昭和町2-7-1 7B 03-5901-9551	一級建築士／341632 中村 司	2025.07.	（仮称）ホンダカーズ 東葛 南柏店　改修工事	１階平面詳細図	1:100	Ａ−０３